©2022 KINLIN RUTHERFURD ARCHITECTS PLLC

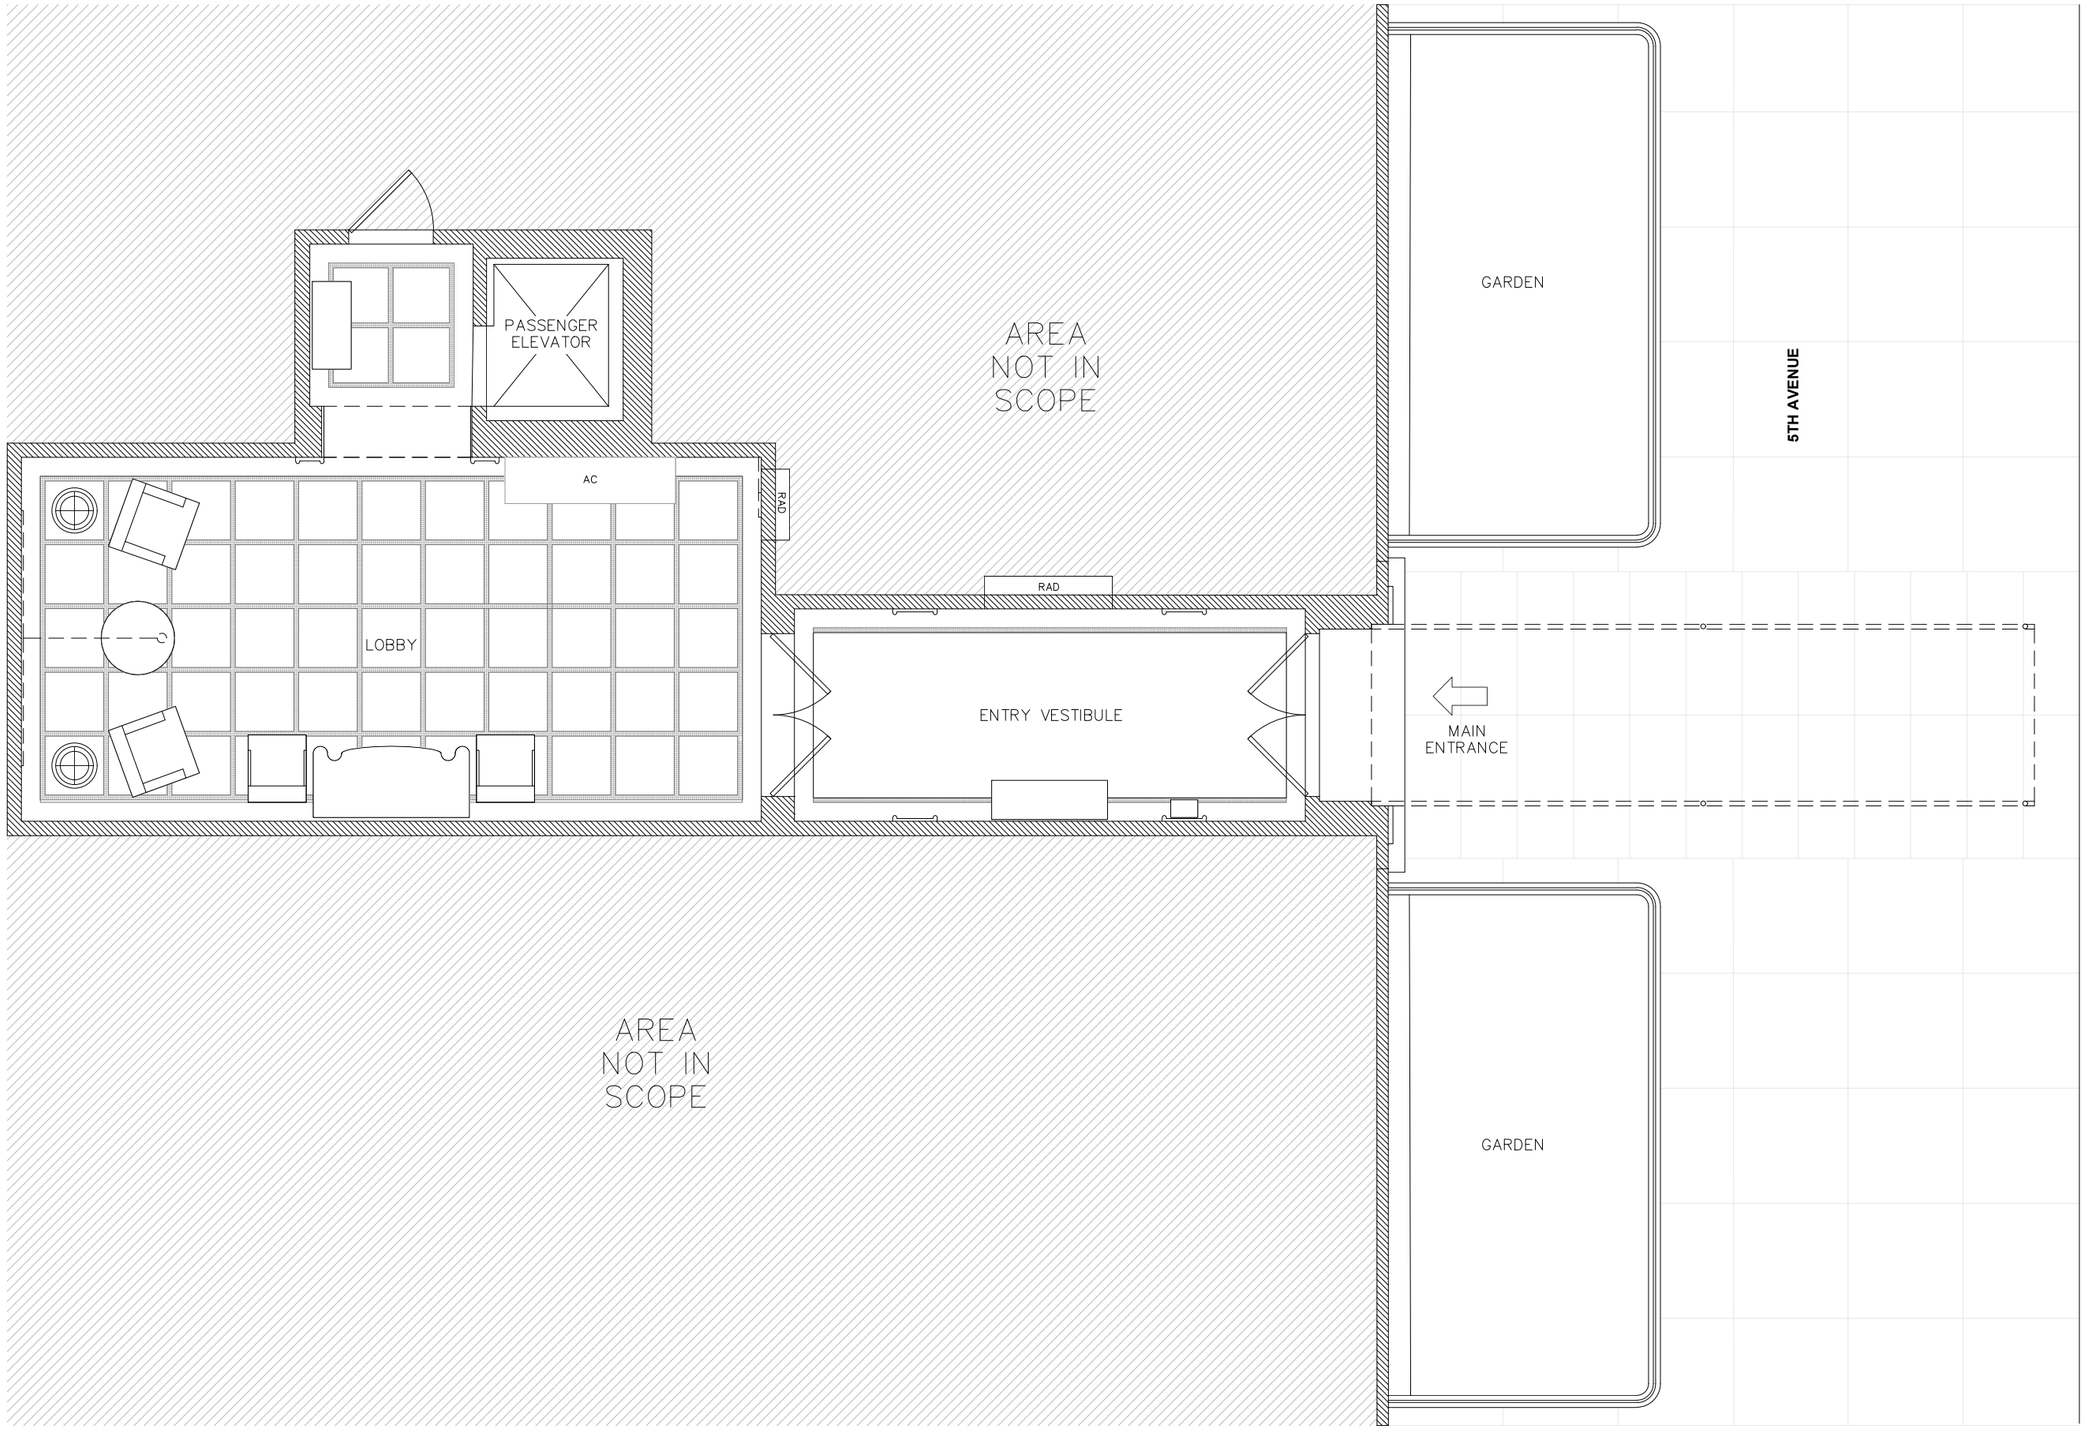

01 GROUND FLOOR PLAN
1/2"=1'-0"

TBD XX.XX.XX

1125 FIFTH AVENUE LOBBY

1125 FIFTH AVENUE
NEW YORK, NY 10128

KINLIN RUTHERFURD ARCHITECTS, PLLC

59 EAST 54TH STREET, SUITE 92
NEW YORK, NEW YORK 10022
TEL: (212) 695-2988

GROUND FLOOR PLAN

PROJECT: 380

A-101

ORIGINAL SHEET SIZE: 22" X 34"

©2023 KINLIN RUTHERFURD ARCHITECTS PLLC

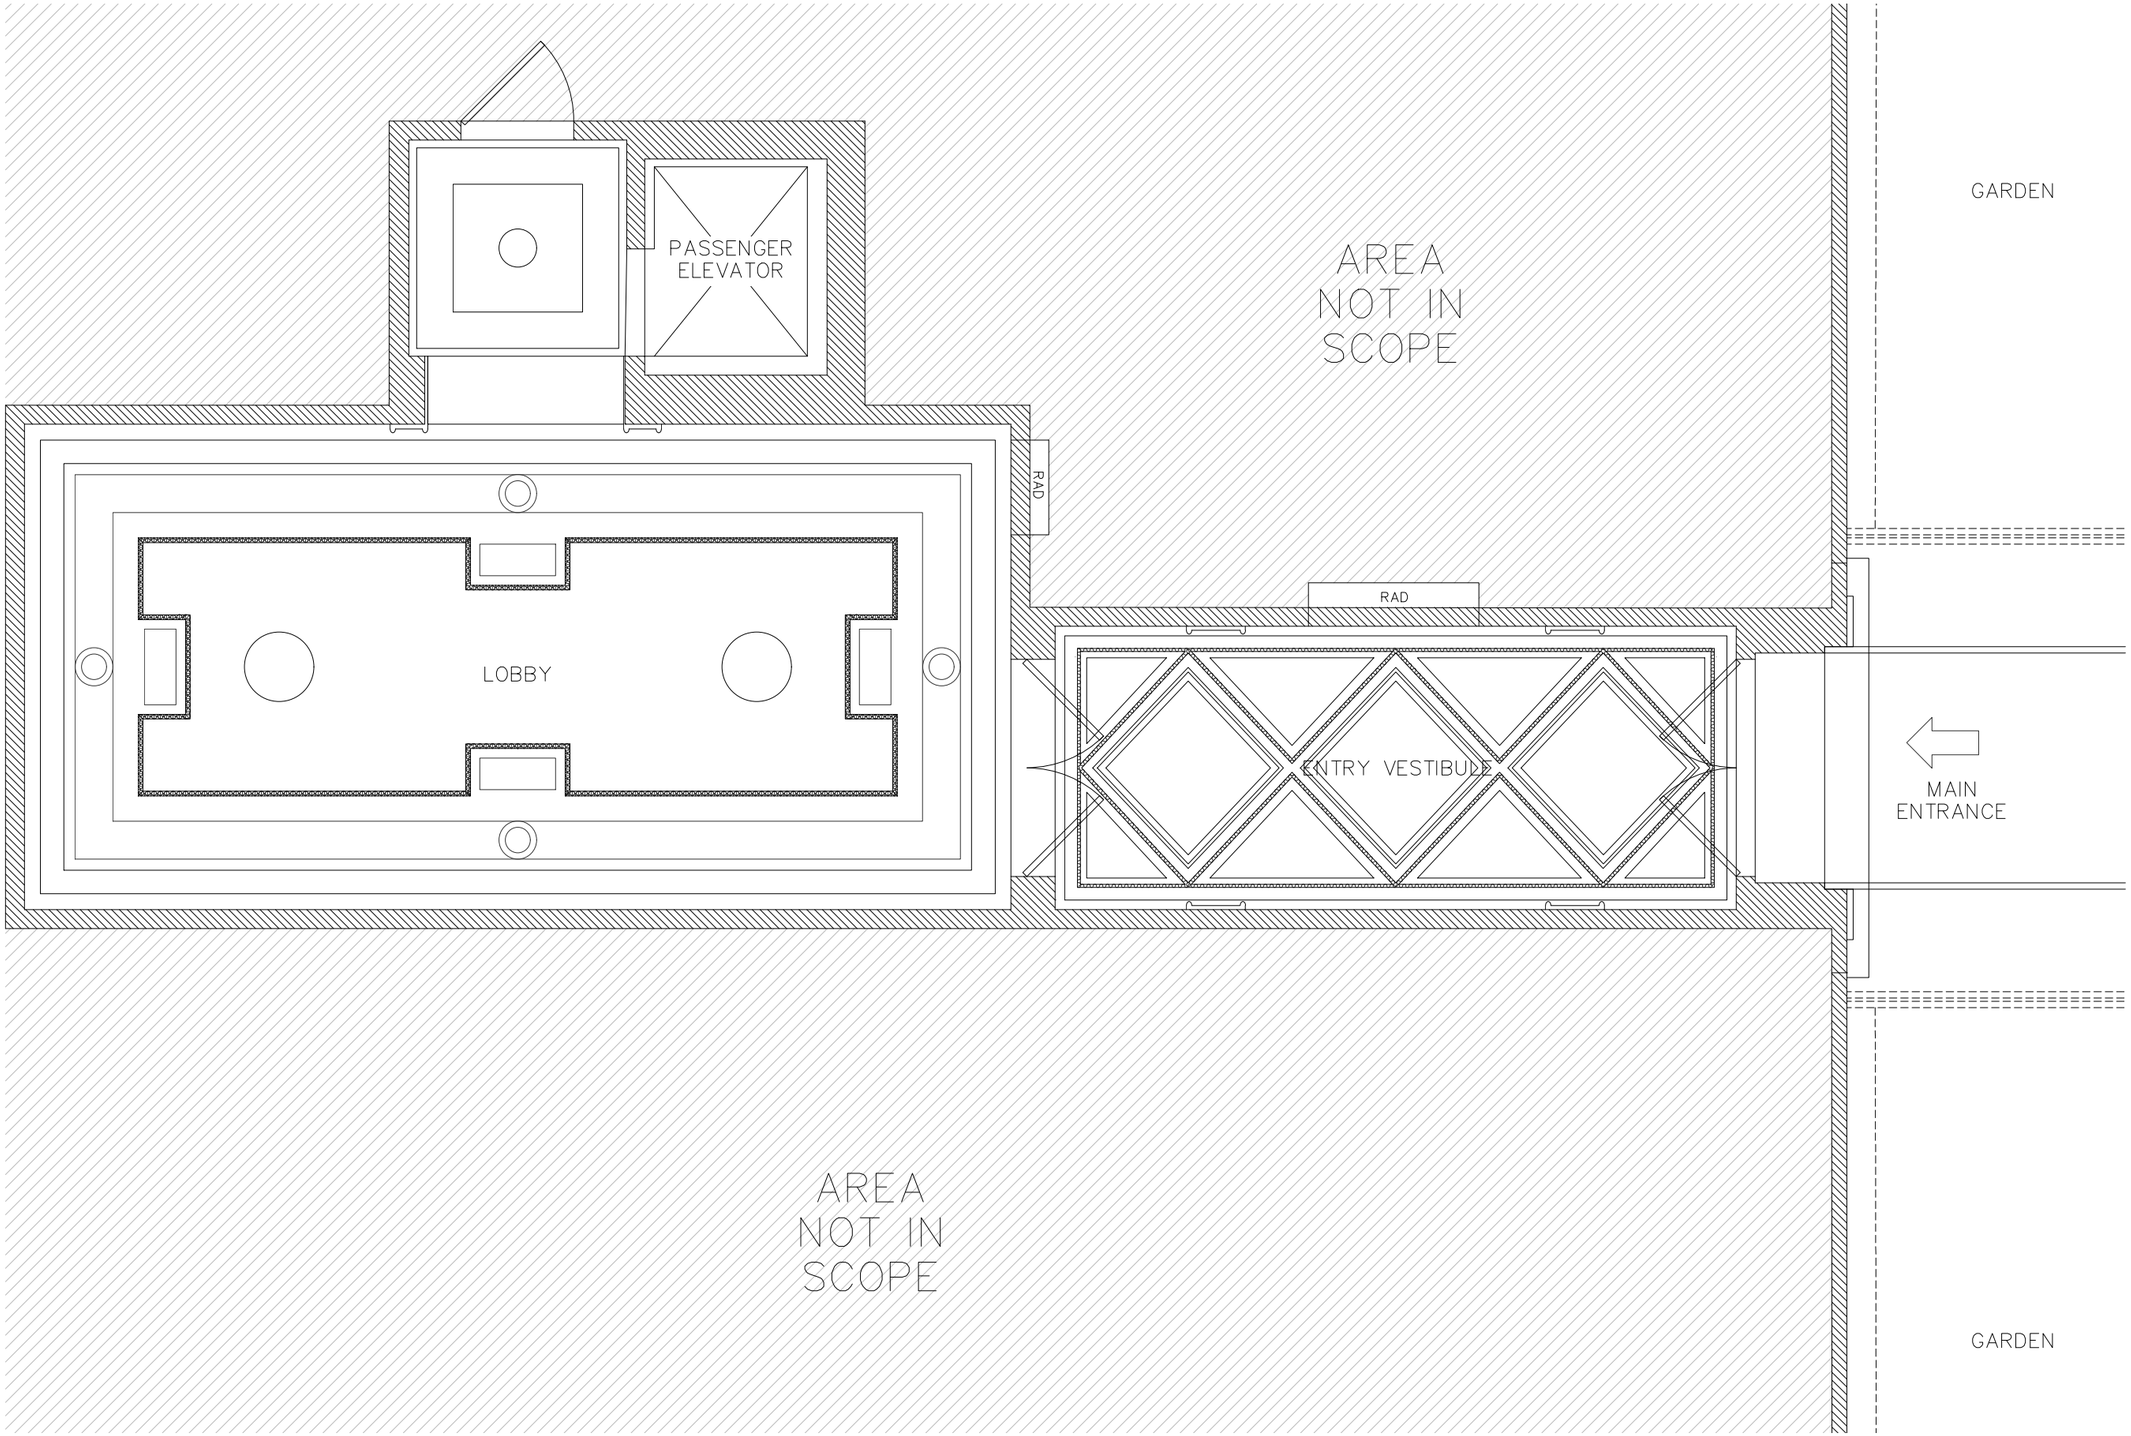

01 GROUND FLOOR PLAN
1/2"=1'-0"

ORIGINAL SHEET SIZE: 22" X 34"

TBD XX.XX.XX

1125 FIFTH AVENUE LOBBY

1125 FIFTH AVENUE
NEW YORK, NY 10128

KINLIN RUTHERFURD ARCHITECTS, PLLC

59 EAST 54TH STREET, SUITE 92
NEW YORK, NEW YORK 10022
TEL: (212) 695-2988

REFLECTED CEILING PLAN

PROJECT: 380

A-111

©2022 KINLIN RUTHERFURD ARCHITECTS PLLC

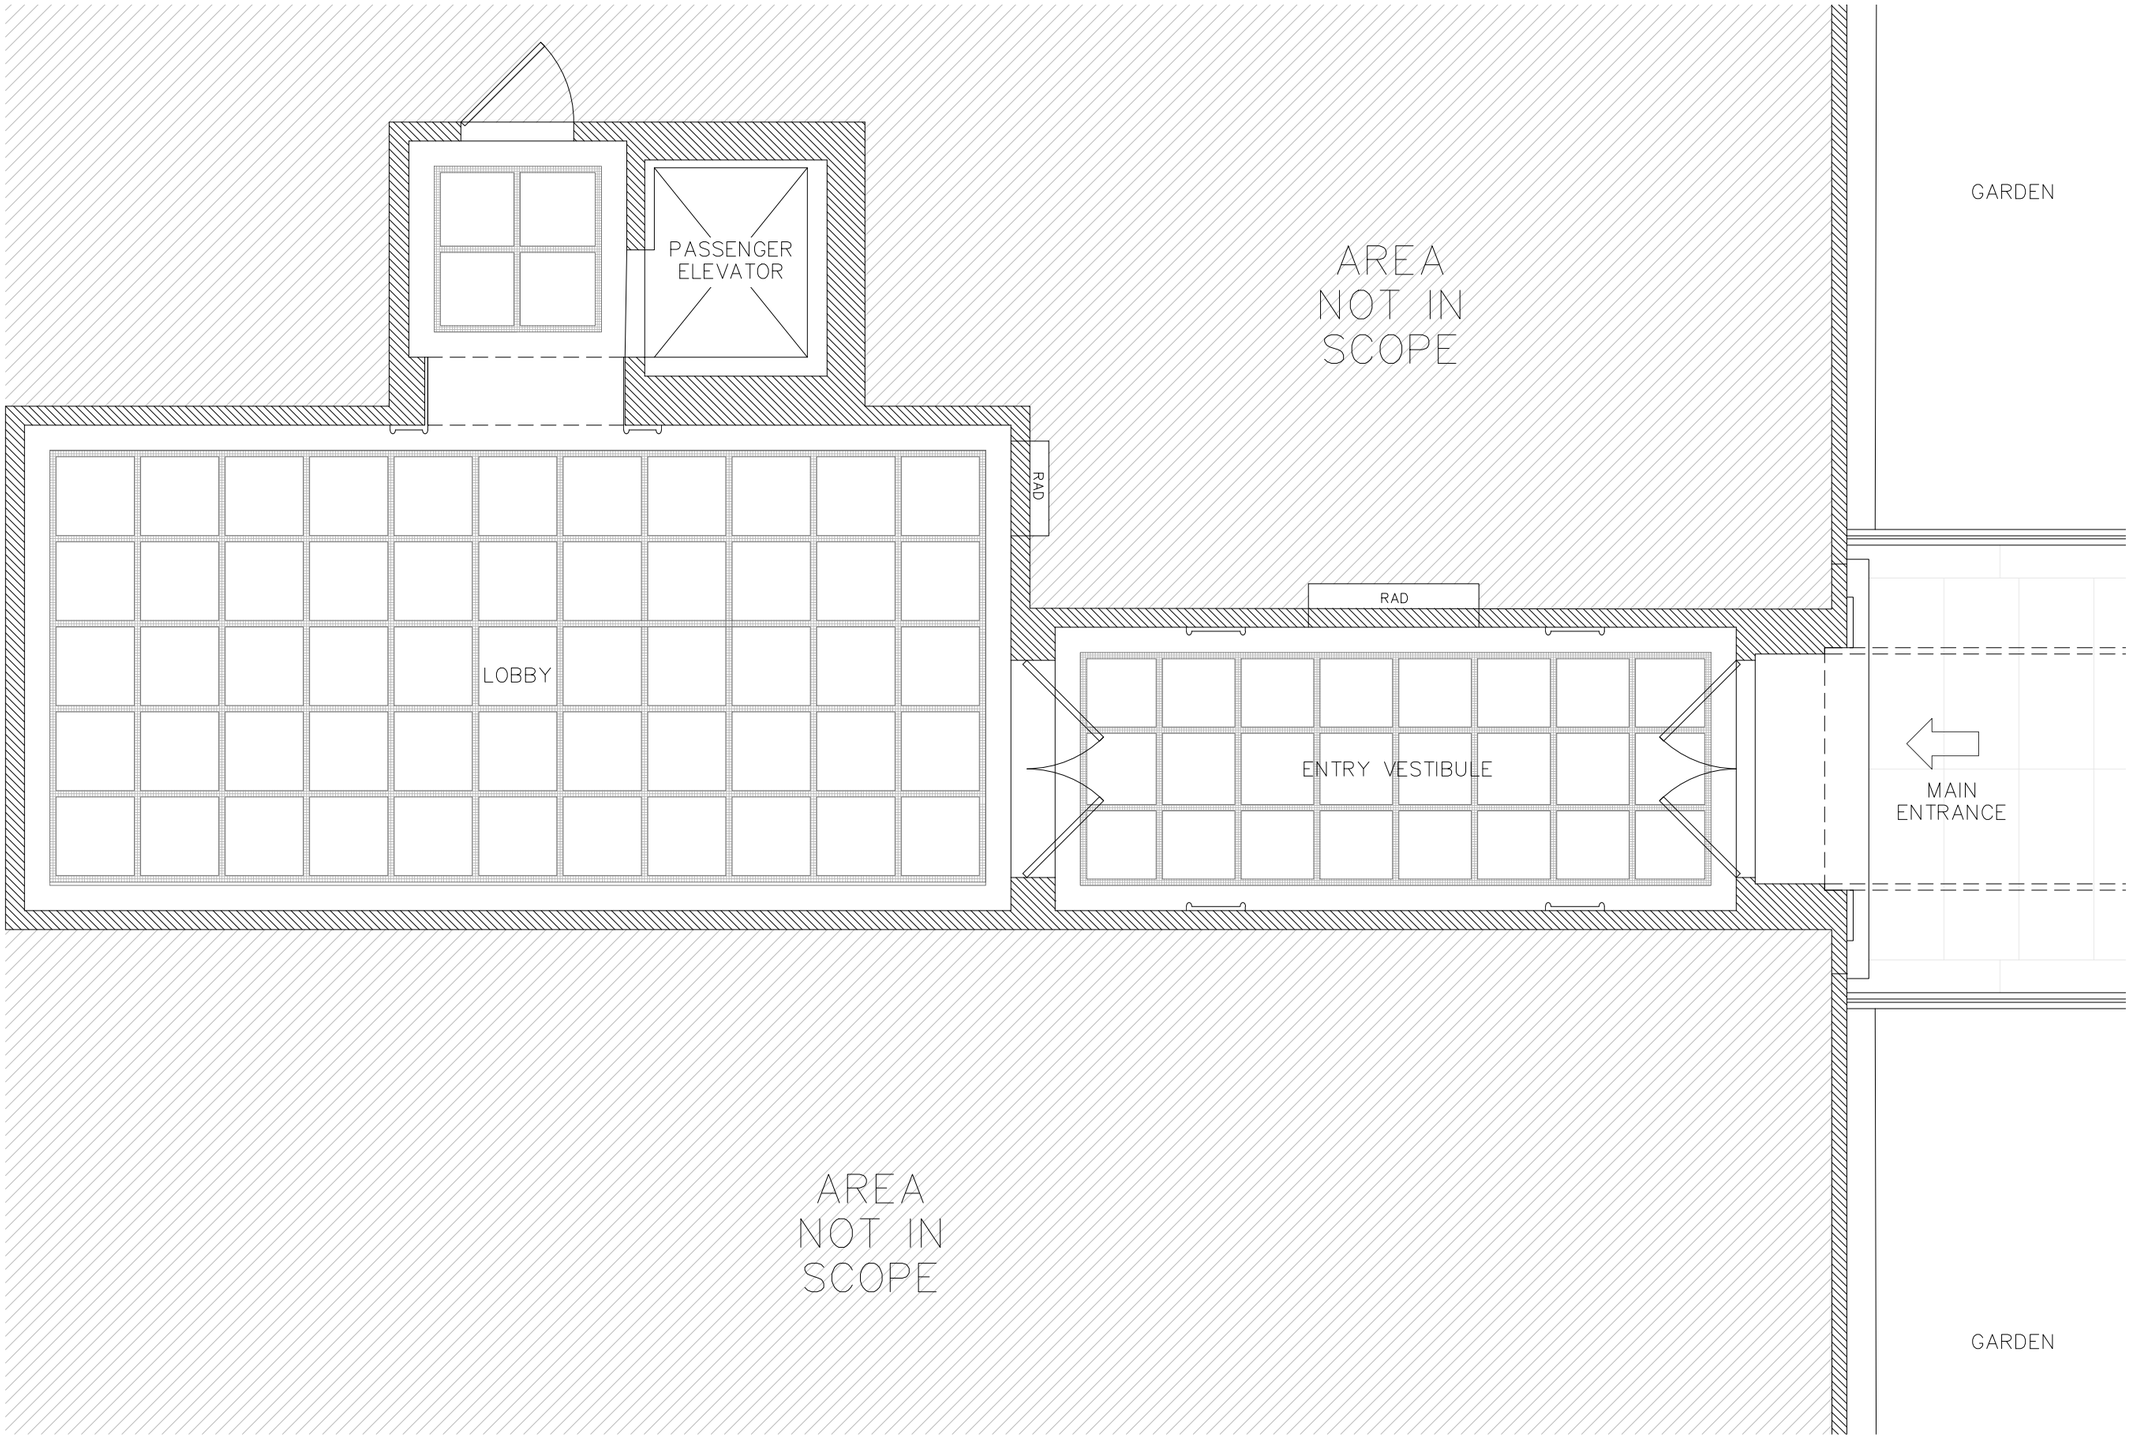

01 GROUND FLOOR PLAN
1/2"=1'-0"

TBD XX.XX.XX

1125 FIFTH AVENUE LOBBY

1125 FIFTH AVENUE
NEW YORK, NY 10128

KINLIN RUTHERFURD ARCHITECTS, PLLC

59 EAST 54TH STREET, SUITE 92
NEW YORK, NEW YORK 10022
TEL: (212) 695-2988

FINISH PLAN

PROJECT: 380

A-131

ORIGINAL SHEET SIZE: 22" X 34"

©2022 KINLIN RUTHERFURD ARCHITECTS PLLC

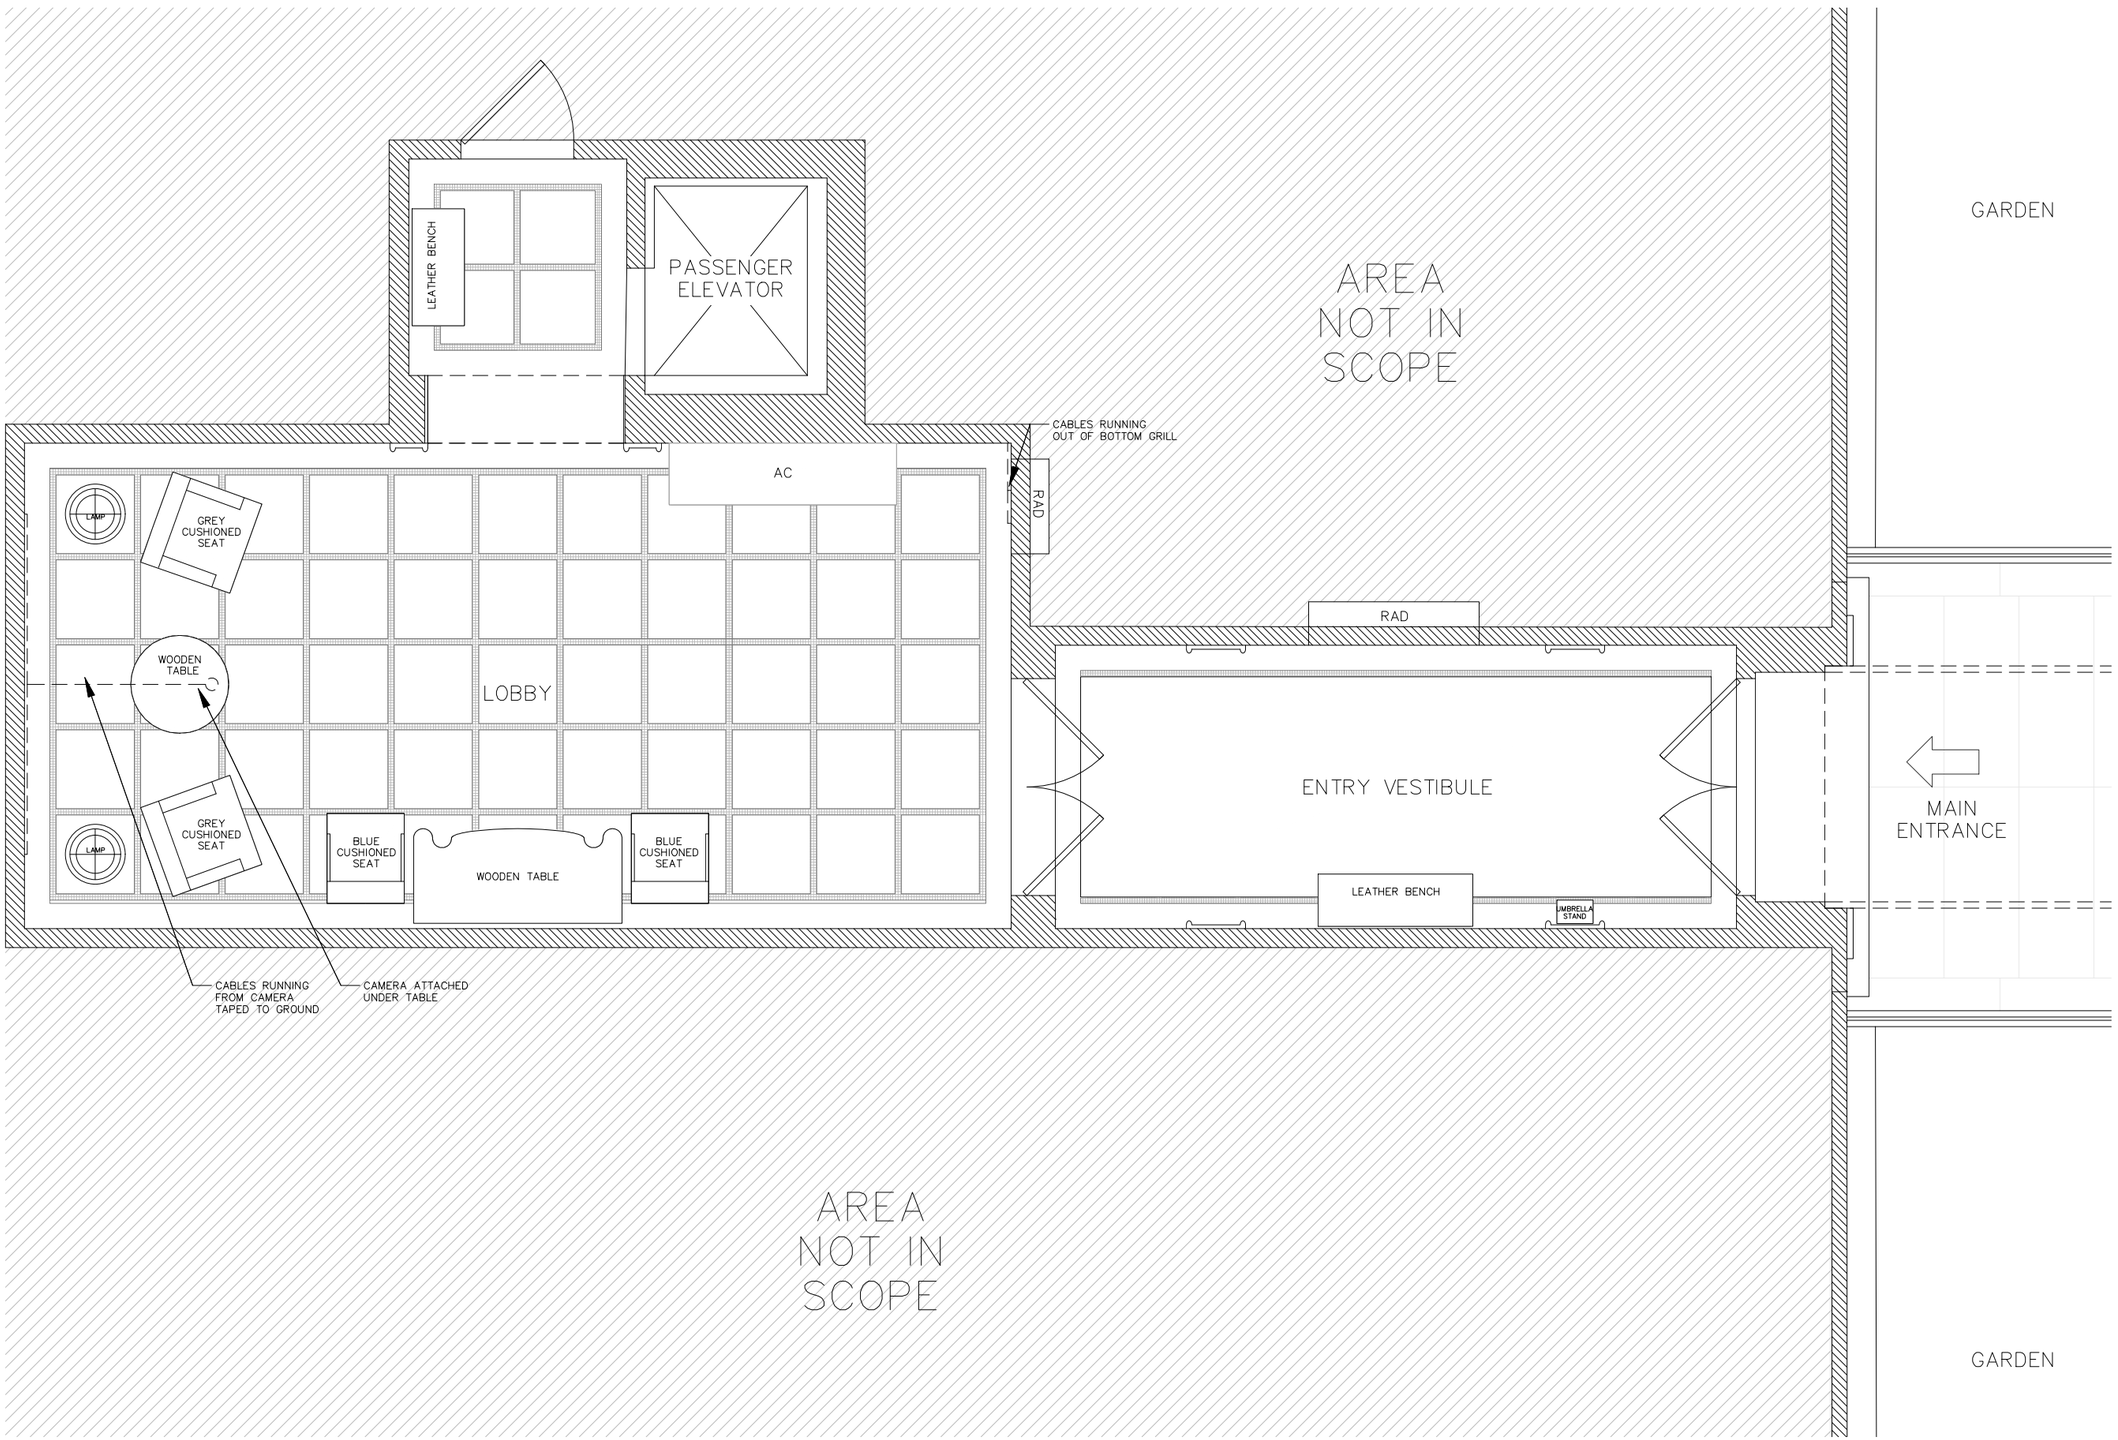

01 GROUND FLOOR PLAN
1/2"=1'-0"

TBD XX.XX.XX

1125 FIFTH AVENUE LOBBY

1125 FIFTH AVENUE
NEW YORK, NY 10128

KINLIN RUTHERFURD ARCHITECTS, PLLC

59 EAST 54TH STREET, SUITE 92
NEW YORK, NEW YORK 10022
TEL: (212) 695-2988

FURNITURE PLAN

PROJECT: 380

A-151

ORIGINAL SHEET SIZE: 22" X 34"

©2022 KINLIN RUTHERFURD ARCHITECTS PLLC

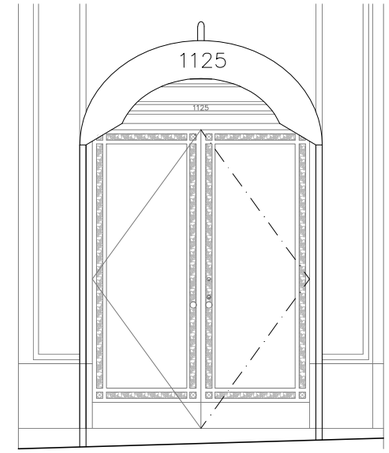

03 WEST ELEVATION
1/2"=1'-0"

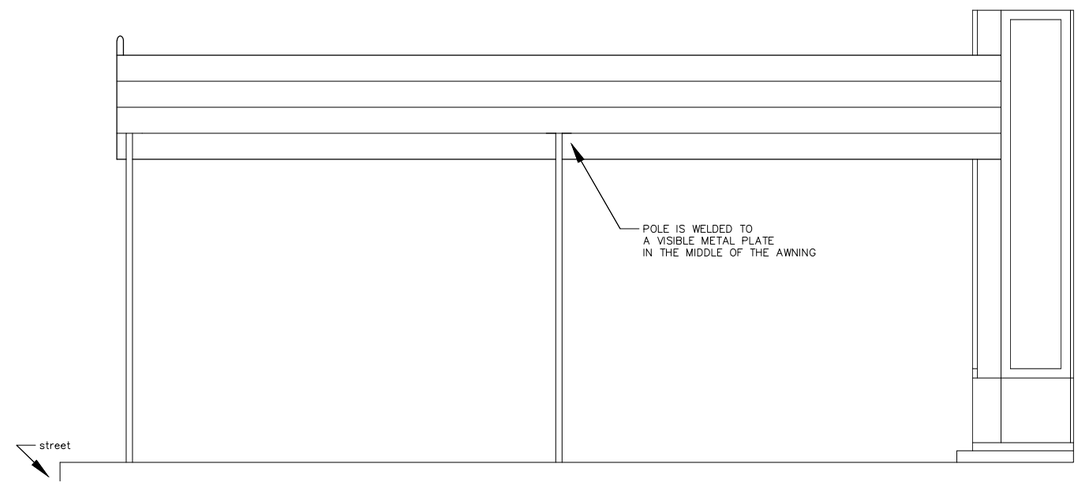

02 NORTH ELEVATION
1/2"=1'-0"

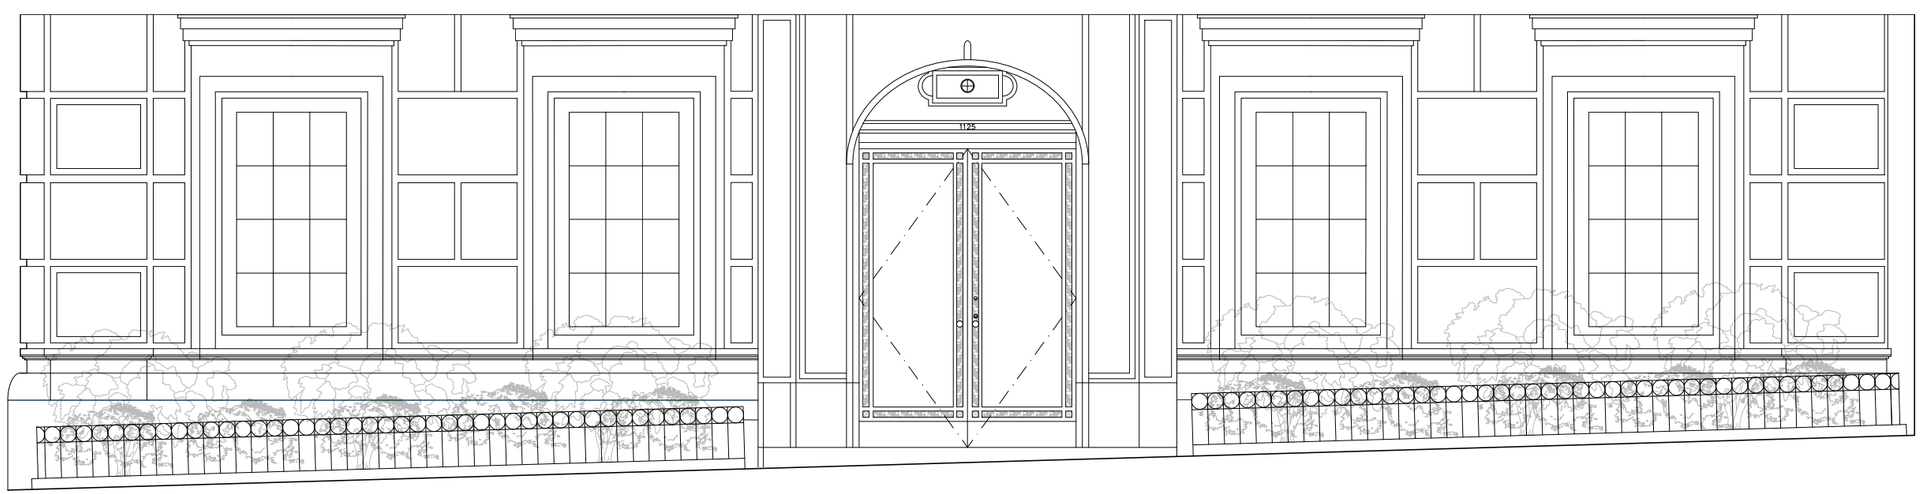

01 WEST ELEVATION
1/2"=1'-0"

TBD XX.XX.XX

1125 FIFTH AVENUE LOBBY

1125 FIFTH AVENUE
NEW YORK, NY 10128

KINLIN RUTHERFURD ARCHITECTS, PLLC

59 EAST 54TH STREET, SUITE 92
NEW YORK, NEW YORK 10022
TEL: (212) 695-2988

EXTERIOR ELEVATION

PROJECT: 380

A-201

ORIGINAL SHEET SIZE: 22" X 34"

©2022 KINLIN RUTHERFURD ARCHITECTS PLLC

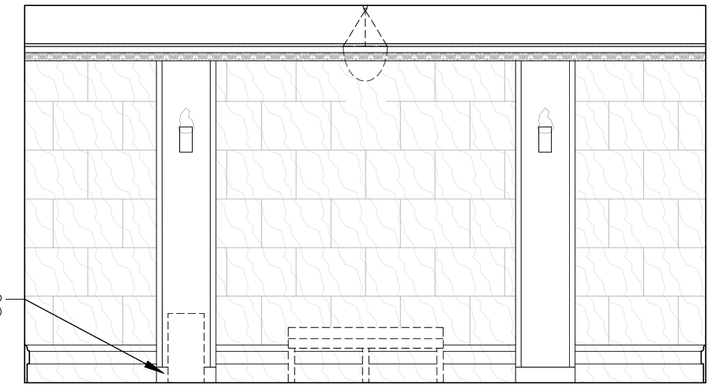

05 NORTH ELEVATION
1/2"=1'-0"

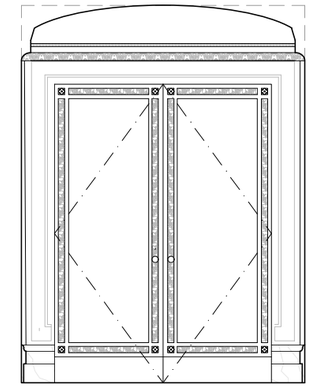

04 EAST ELEVATION
1/2"=1'-0"

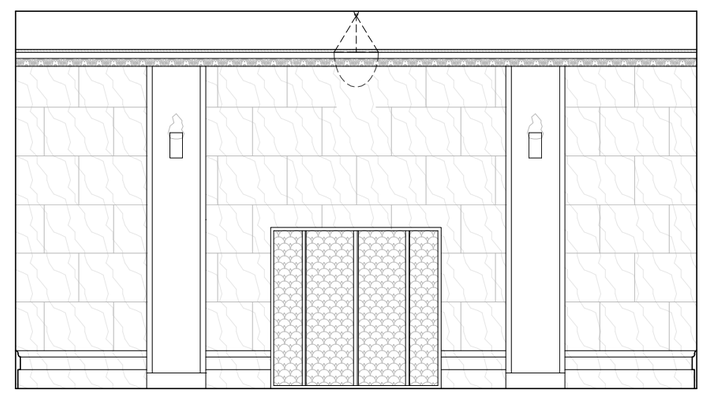

03 SOUTH ELEVATION
1/2"=1'-0"

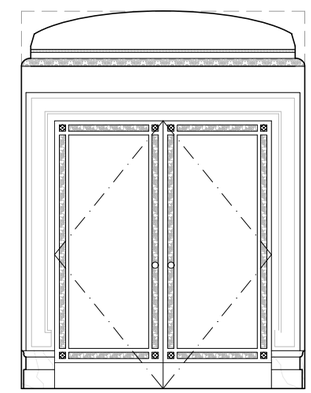

02 WEST ELEVATION
1/2"=1'-0"

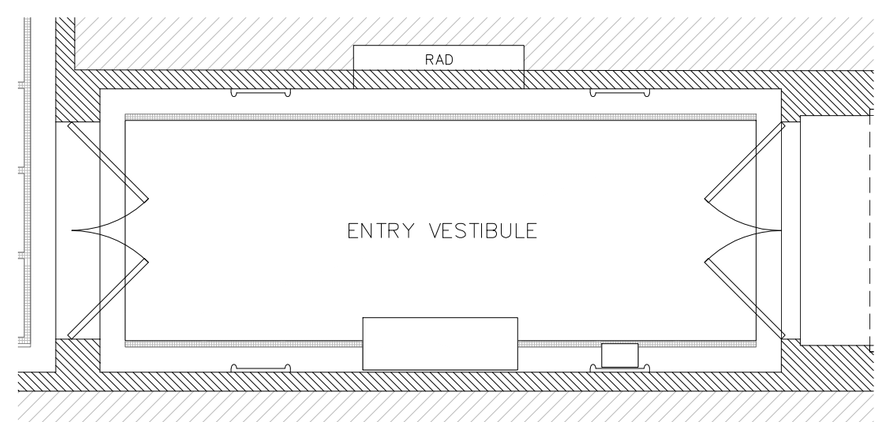

01 KEY PLAN
1/2"=1'-0"

TBD XX.XX.XX

1125 FIFTH AVENUE LOBBY

1125 FIFTH AVENUE
NEW YORK, NY 10128

KINLIN RUTHERFURD ARCHITECTS, PLLC

59 EAST 54TH STREET, SUITE 92
NEW YORK, NEW YORK 10022
TEL: (212) 695-2988

INTERIOR ELEVATIONS VESTIBULE

PROJECT: 380

A-301

ORIGINAL SHEET SIZE: 22" X 34"

©2022 KINLIN RUTHERFURD ARCHITECTS PLLC

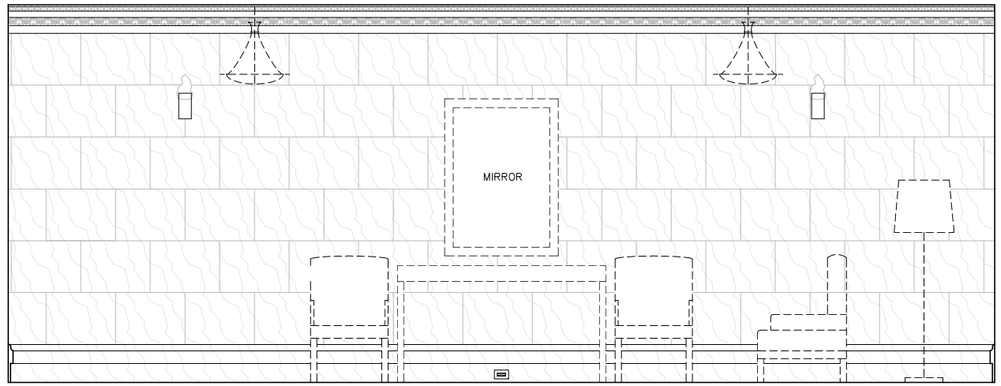

05 NORTH ELEVATION
1/2"=1'-0"

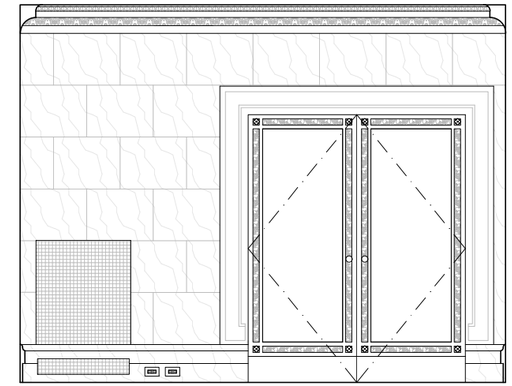

04 EAST ELEVATION
1/2"=1'-0"

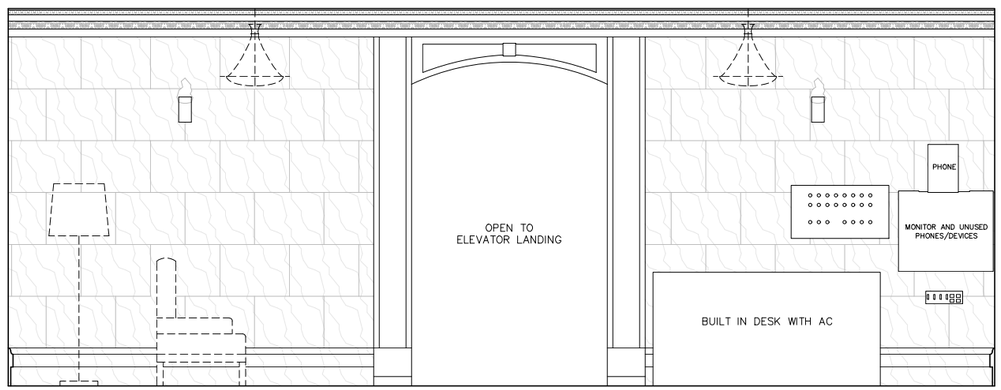

03 SOUTH ELEVATION
1/2"=1'-0"

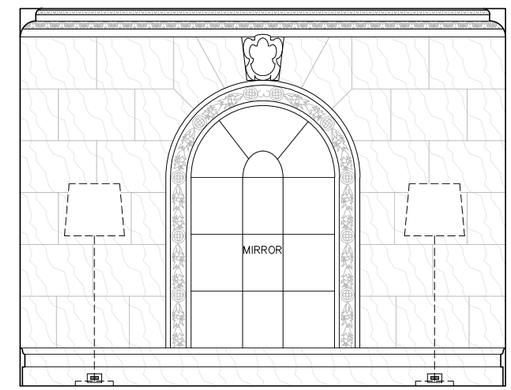

02 WEST ELEVATION
1/2"=1'-0"

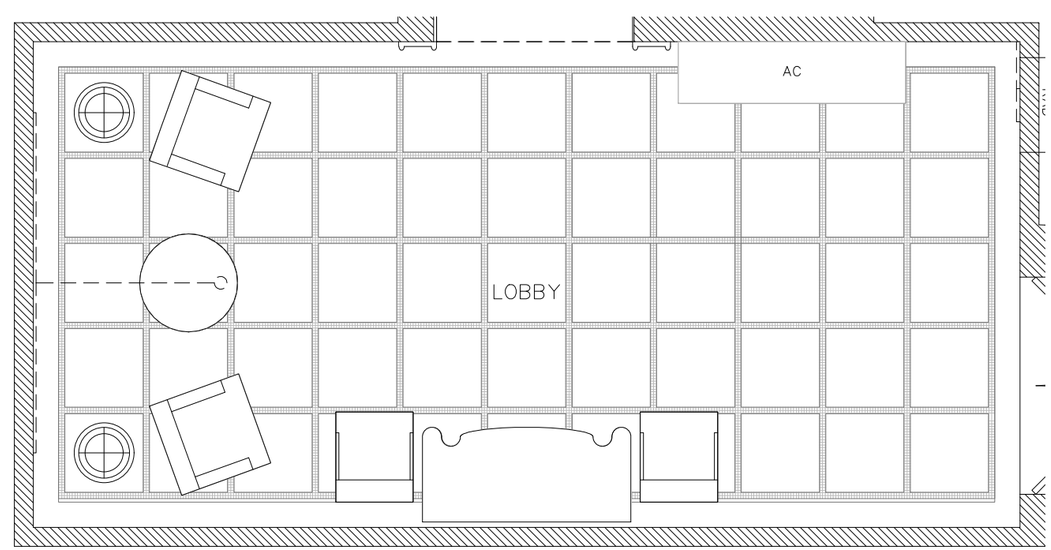

01 KEY PLAN
1/2"=1'-0"

REVISION	ISSUE	DATE
	TBD	XX.XX.XX

1125 FIFTH AVENUE LOBBY

1125 FIFTH AVENUE
NEW YORK, NY 10128

KINLIN RUTHERFURD ARCHITECTS, PLLC
59 EAST 54TH STREET, SUITE 92
NEW YORK, NEW YORK 10022
TEL: (212) 695-2988

INTERIOR ELEVATIONS LOBBY

A-302

PROJECT: 380

ORIGINAL SHEET SIZE: 22" X 34"

©2022 KINLIN RUTHERFURD ARCHITECTS PLLC

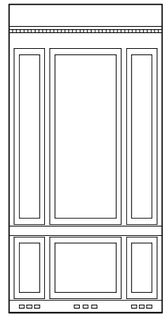

09 NORTH ELEVATION
1/2"=1'-0"

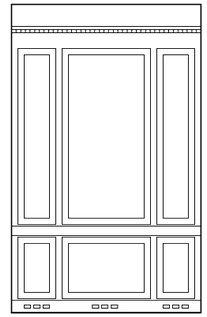

08 EAST ELEVATION
1/2"=1'-0"

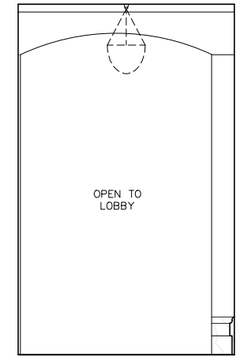

07 NORTH ELEVATION
1/2"=1'-0"

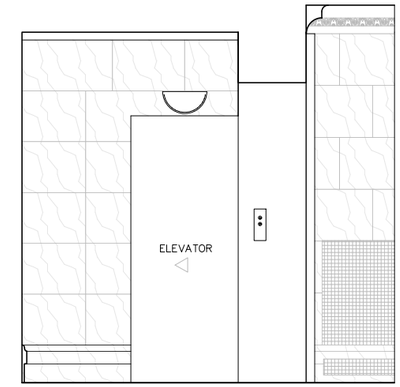

06 EAST ELEVATION
1/2"=1'-0"

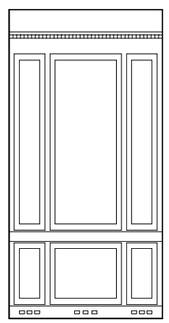

05 SOUTH ELEVATION
1/2"=1'-0"

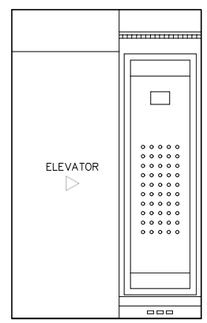

04 WEST ELEVATION
1/2"=1'-0"

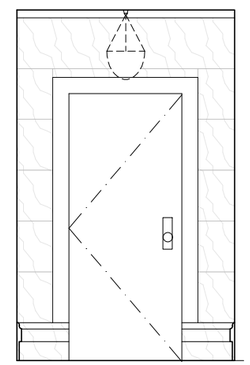

03 SOUTH ELEVATION
1/2"=1'-0"

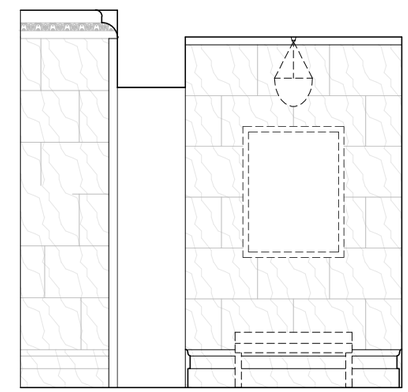

02 WEST ELEVATION
1/2"=1'-0"

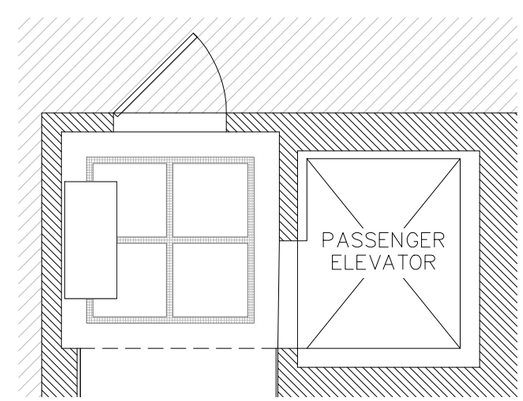

01 KEY PLAN
1/2"=1'-0"

TBD XX.XX.XX

1125 FIFTH AVENUE LOBBY

1125 FIFTH AVENUE
NEW YORK, NY 10128

KINLIN RUTHERFURD ARCHITECTS, PLLC

59 EAST 54TH STREET, SUITE 92
NEW YORK, NEW YORK 10022
TEL: (212) 695-2988

INTERIOR ELEVATIONS
ELEVATOR LANDING

PROJECT: 380

A-303

ORIGINAL SHEET SIZE: 22" X 34"